HELENE SELMER
GENERAL ARRANGEMENT

SCALE 1:200

PLAN HISTORY	
7TH OCT., 2002	PREPARED FOR EX-ST56BC
17TH DEC., 2002	PREPARED FOR CONTRACT
23TH JUN., 2004	PREPARED FOR APPROVAL
28TH FEB., 2005	PREPARED FOR FINISHED PLAN

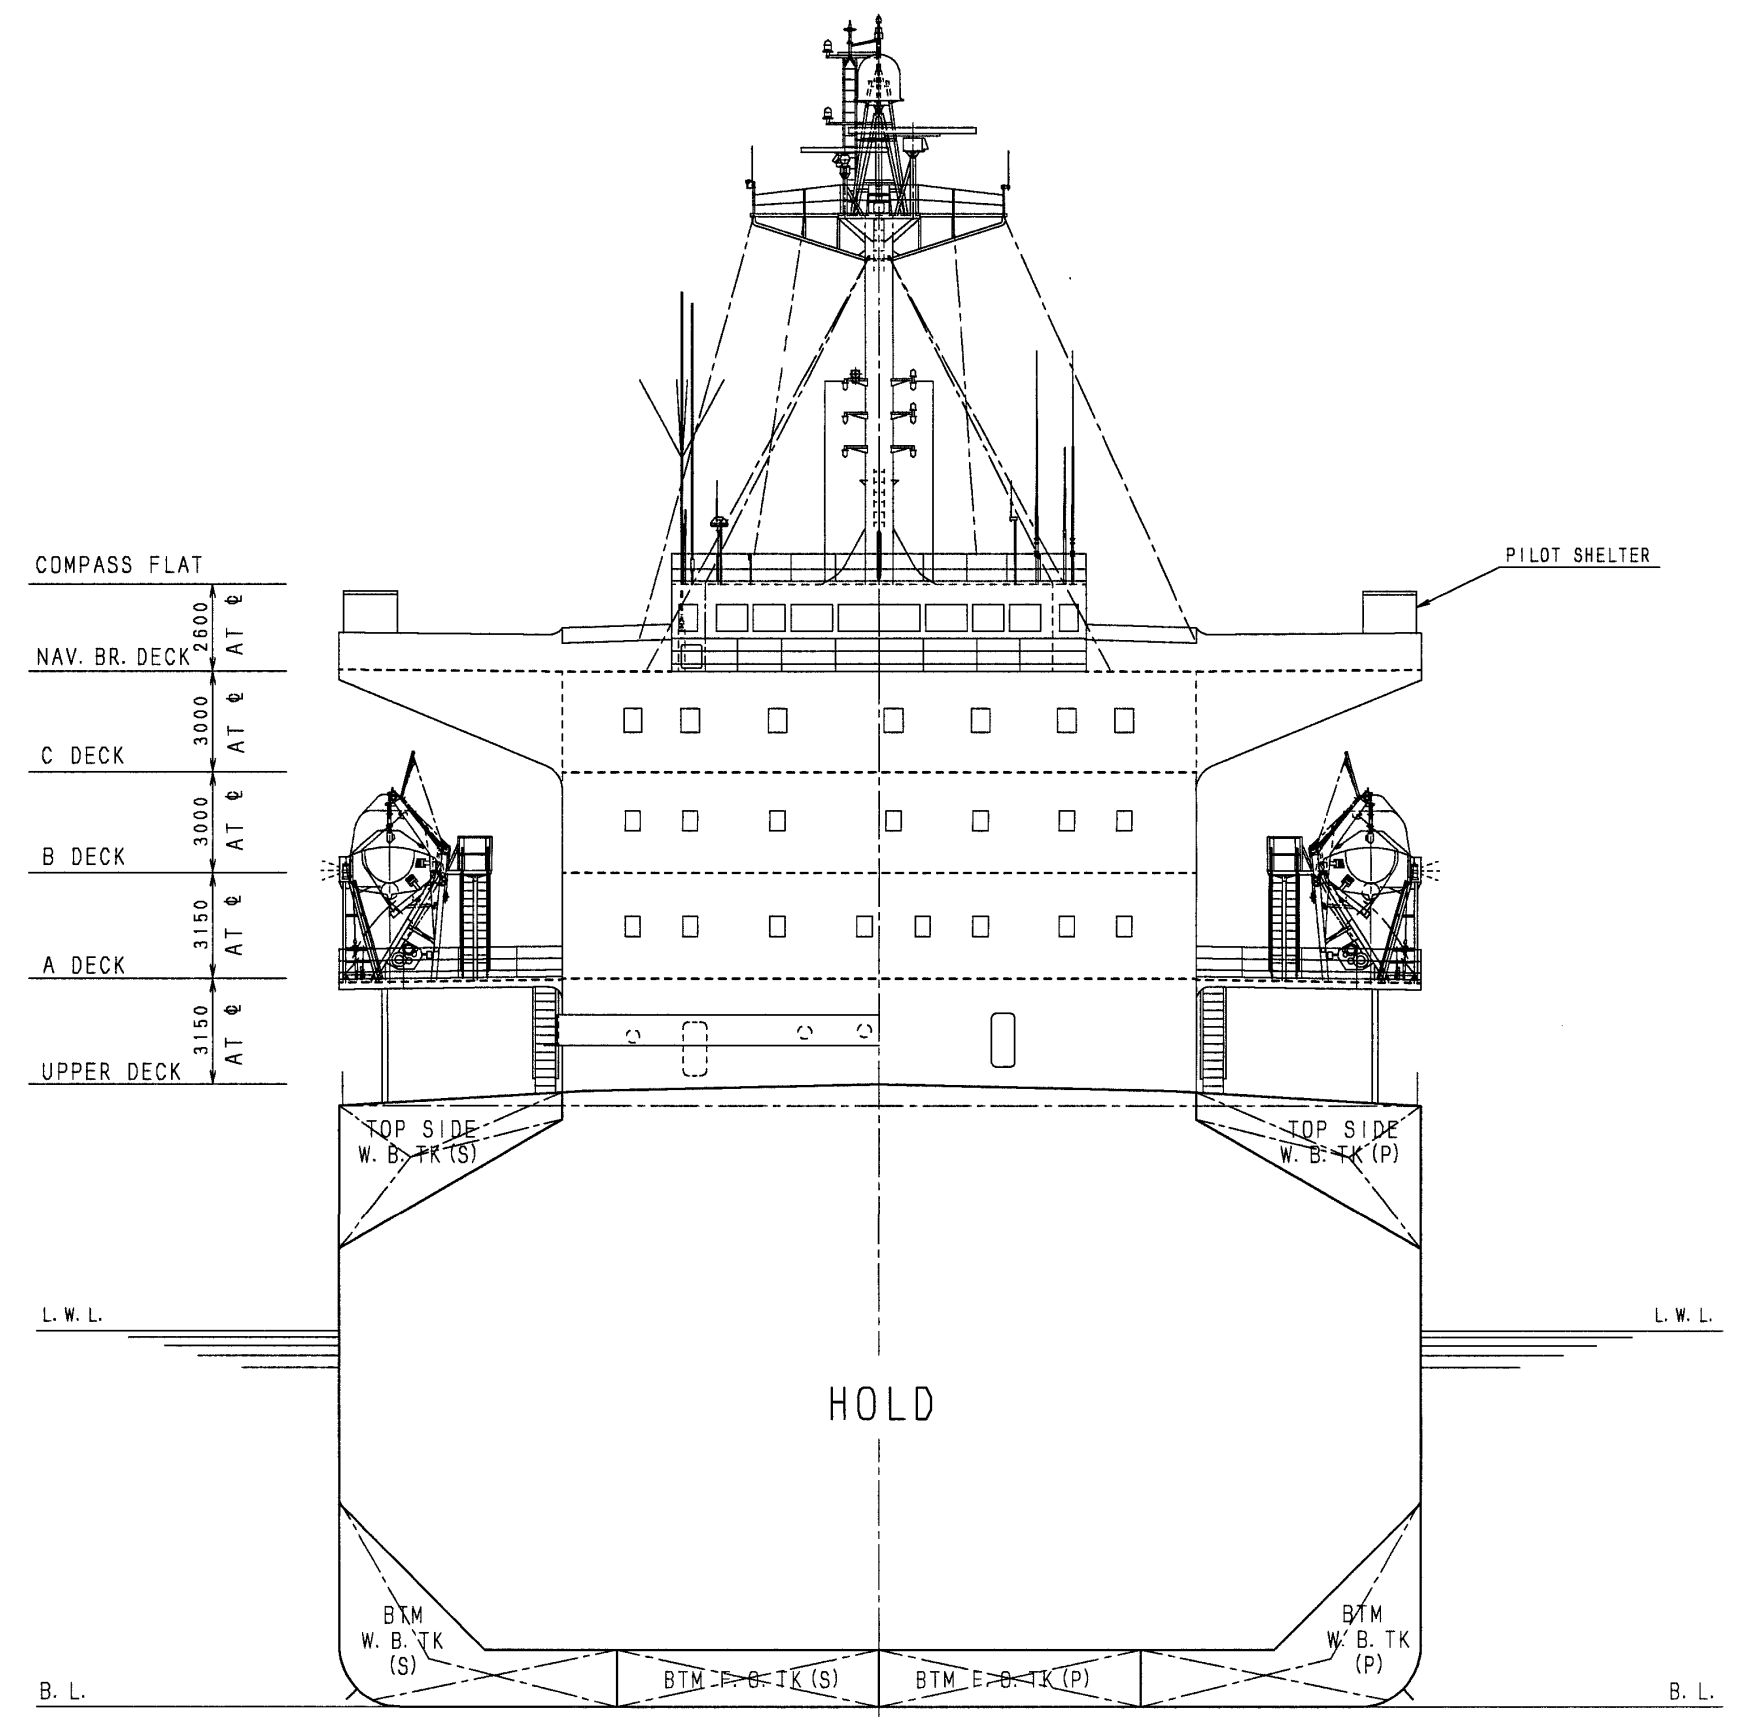
COMPASS FLAT
NAV. BR. DECK
C DECK
B DECK
A DECK
UPPER DECK
PILOT SHELTER
HOLD
L.W.L.
B.L.

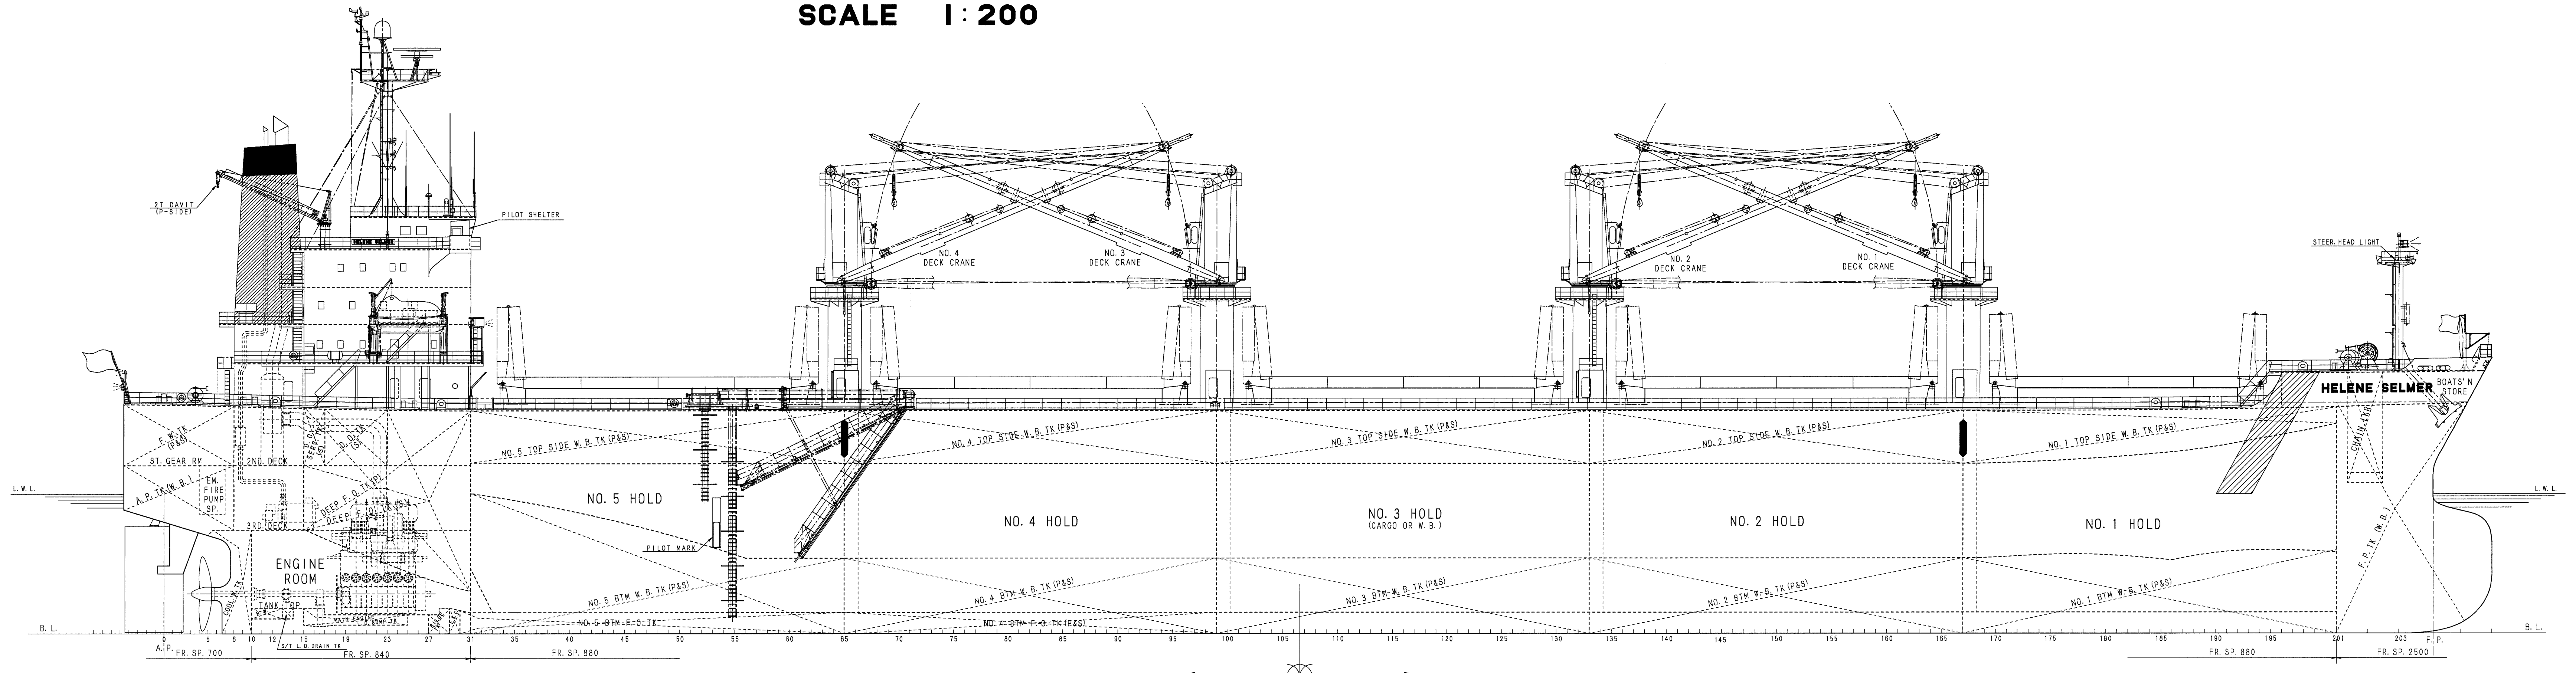
2T DAVIT (P-SIDE)
PILOT SHELTER
NO. 4 DECK CRANE
NO. 3 DECK CRANE
NO. 2 DECK CRANE
NO. 1 DECK CRANE
STEER. HEAD LIGHT
HELENE SELMER
BOATS'N STORE
F.W.TK (P&S)
ST. GEAR RM
2ND. DECK
A.P. TK (W.B.)
EM. FIRE PUMP SP.
DEEP F.O. TK (P)
DEEP F.O. TK (S)
3RD. DECK
ENGINE ROOM
TANK TOP
COOL. W. TK
NO. 5 TOP SIDE W.B. TK (P&S)
NO. 4 TOP SIDE W.B. TK (P&S)
NO. 3 TOP SIDE W.B. TK (P&S)
NO. 2 TOP SIDE W.B. TK (P&S)
NO. 1 TOP SIDE W.B. TK (P&S)
NO. 5 HOLD
NO. 4 HOLD
NO. 3 HOLD (CARGO OR W.B.)
NO. 2 HOLD
NO. 1 HOLD
PILOT MARK
NO. 5 BTM W.B. TK (P&S)
NO. 4 BTM W.B. TK (P&S)
NO. 3 BTM W.B. TK (P&S)
NO. 2 BTM W.B. TK (P&S)
NO. 1 BTM W.B. TK (P&S)
NO. 5 BTM F.O. TK
NO. 4 BTM F.O. TK (P&S)
CHAIN LKR
F.P. TK (W.B.)
L.W.L.
B.L.
A.P.
F.P.
FR. SP. 700
FR. SP. 840
FR. SP. 880
FR. SP. 2500
S/T L.O. DRAIN TK

PRINCIPAL PARTICULARS		
1.	PRINCIPAL DIMENSIONS	
	LENGTH (O.A.)	189.99 M
	LENGTH (P.P.)	182.00 M
	BREADTH (MLD.)	32.26 M
	DEPTH (MLD.)	17.90 M
	DRAFT (MLD.) DESIGN	11.20 M
	DRAFT (MLD.) SCANTLING	12.55 M
2.	TONNAGE	
	GROSS (INTERNATIONAL)	31,218 M.T.
	NET (INTERNATIONAL)	18,534 M.T.
3.	DEADWEIGHT (DESIGN/SCANTLING)	48,231/55,741 M.T.
4.	MAIN ENGINE	
	TYPE & NO.	MITSUI MAN B&W 6S50MCC 1 SET
	M.C.R.	9,480 kW X 127 RPM.
	N.S.R.	7,080 kW X 115.2 RPM.
5.	SERVICE SPEED	ABT. 14.5 KTS.
	(ON DESIGN DRAFT AT NSR WITH 15% SEA MARGIN)	
6.	COMPLEMENT	TOTAL 24 P.
7.	CLASS	DNV, +1A1, BULK CARRIER, ESP, ES(S), HC-E, HOLDS 2, 4 EMPTY, EO, TMON, GRAIN-U
8.	PORT OF REGISTRY	MAJURO, MARSHAL ISLANDS
9.	OFFICIAL NUMBER	90150
10.	CALL SIGN	V7HD5
11.	OWNER	WEHR BULKCARRIERS GmbH & CO. KG
12.	BUILDER	MITSUI ENGINEERING & SHIPBUILDING CO., LTD., TAMANO WORKS
13.	KEEL LAID	30TH SEP., 2004
14.	LAUNCHED	14TH JAN., 2005
15.	DELIVERED	15TH MAR., 2005

COMP. FLAT

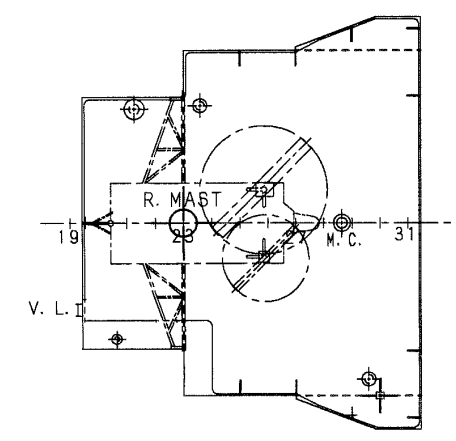

NAV. BRI. DECK

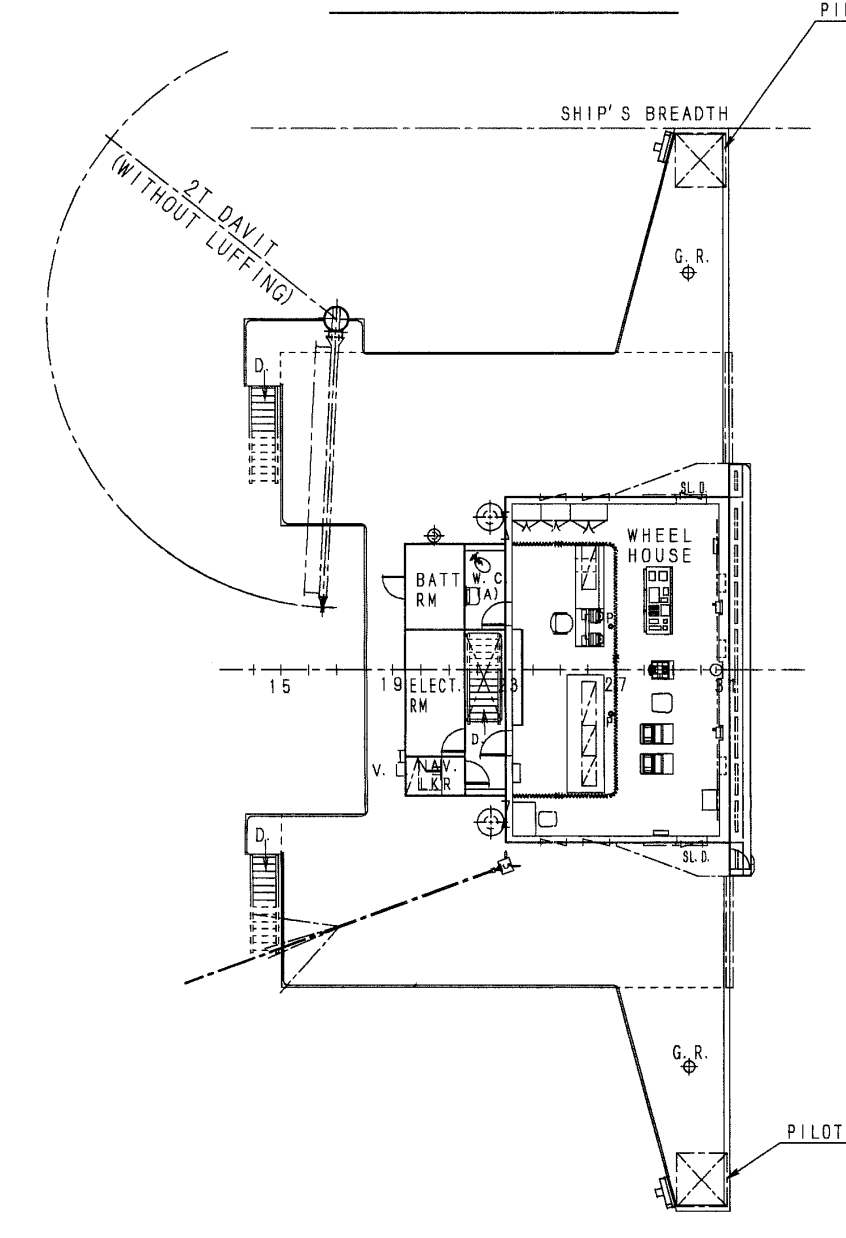
PILOT SHELTER

C DECK

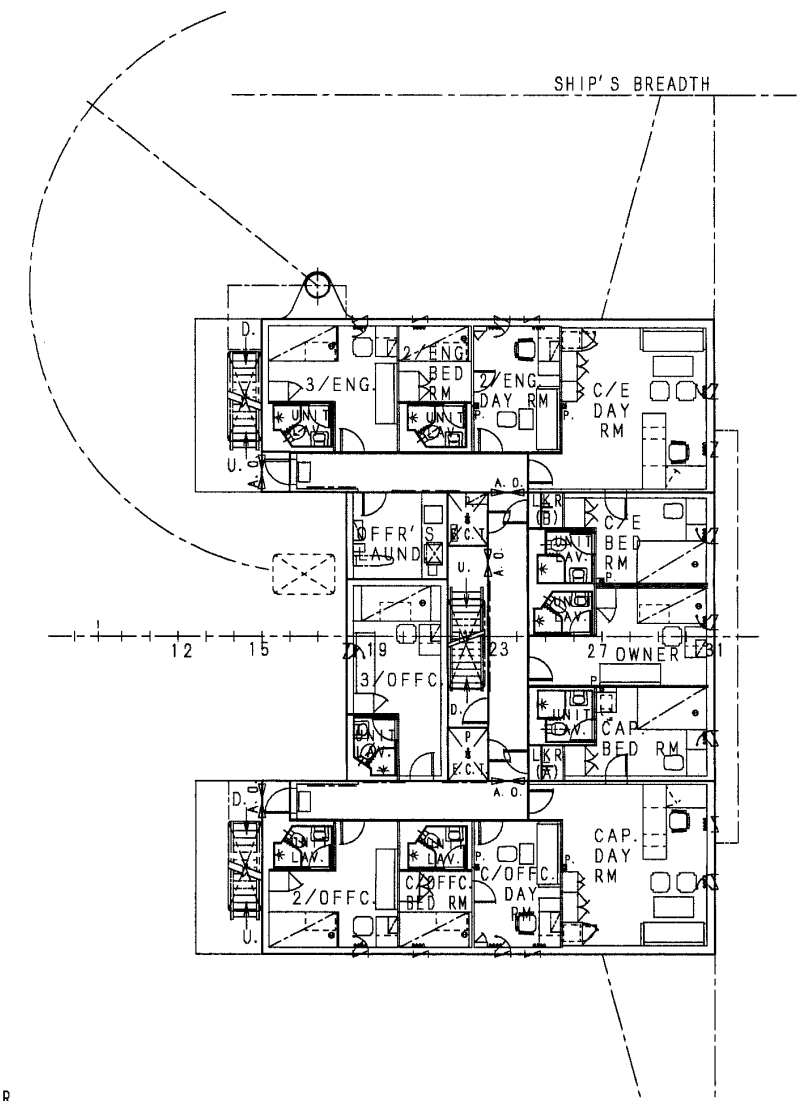

B DECK

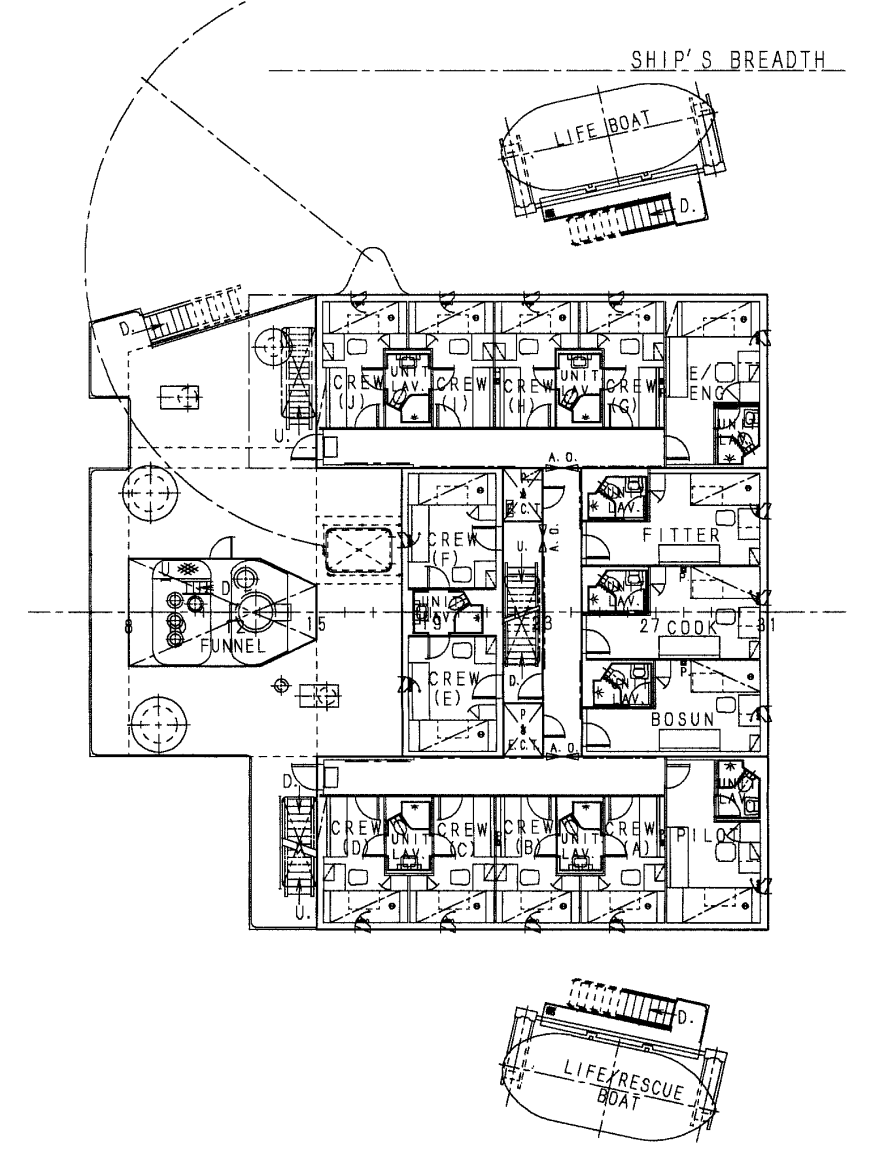

A DECK

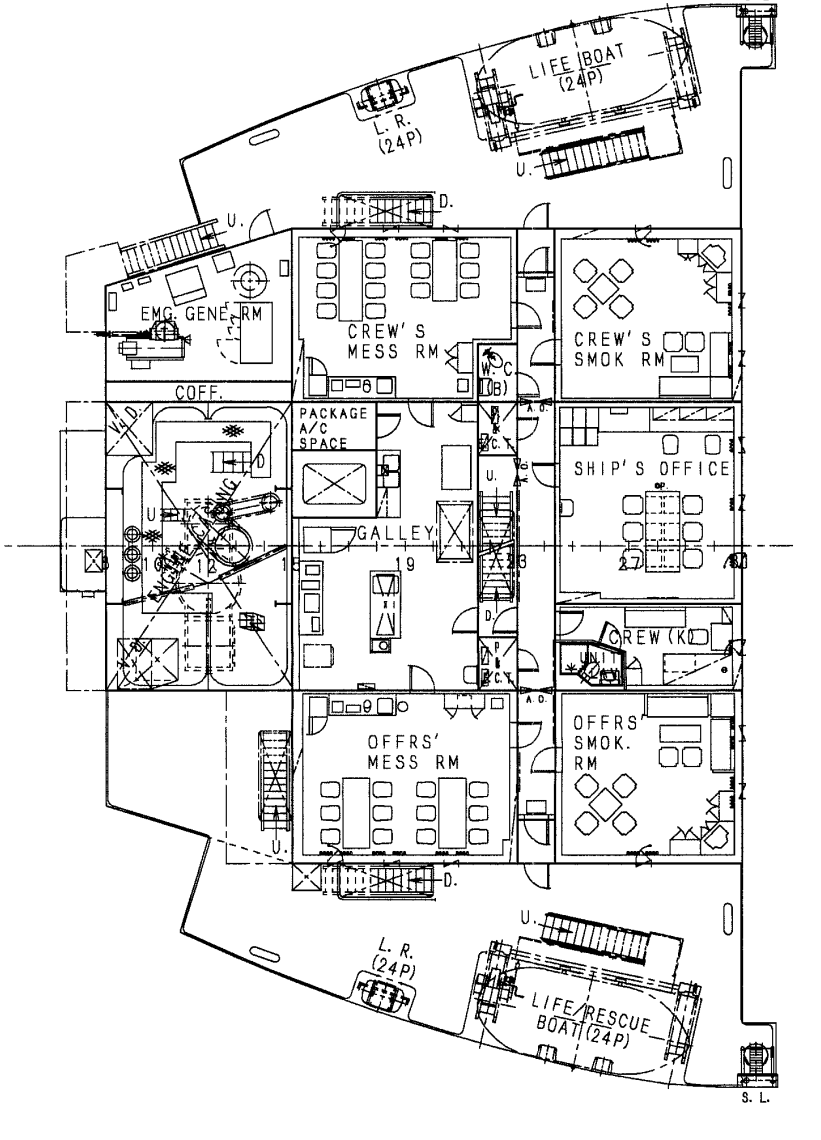

UPP. DECK

UPPER DECK

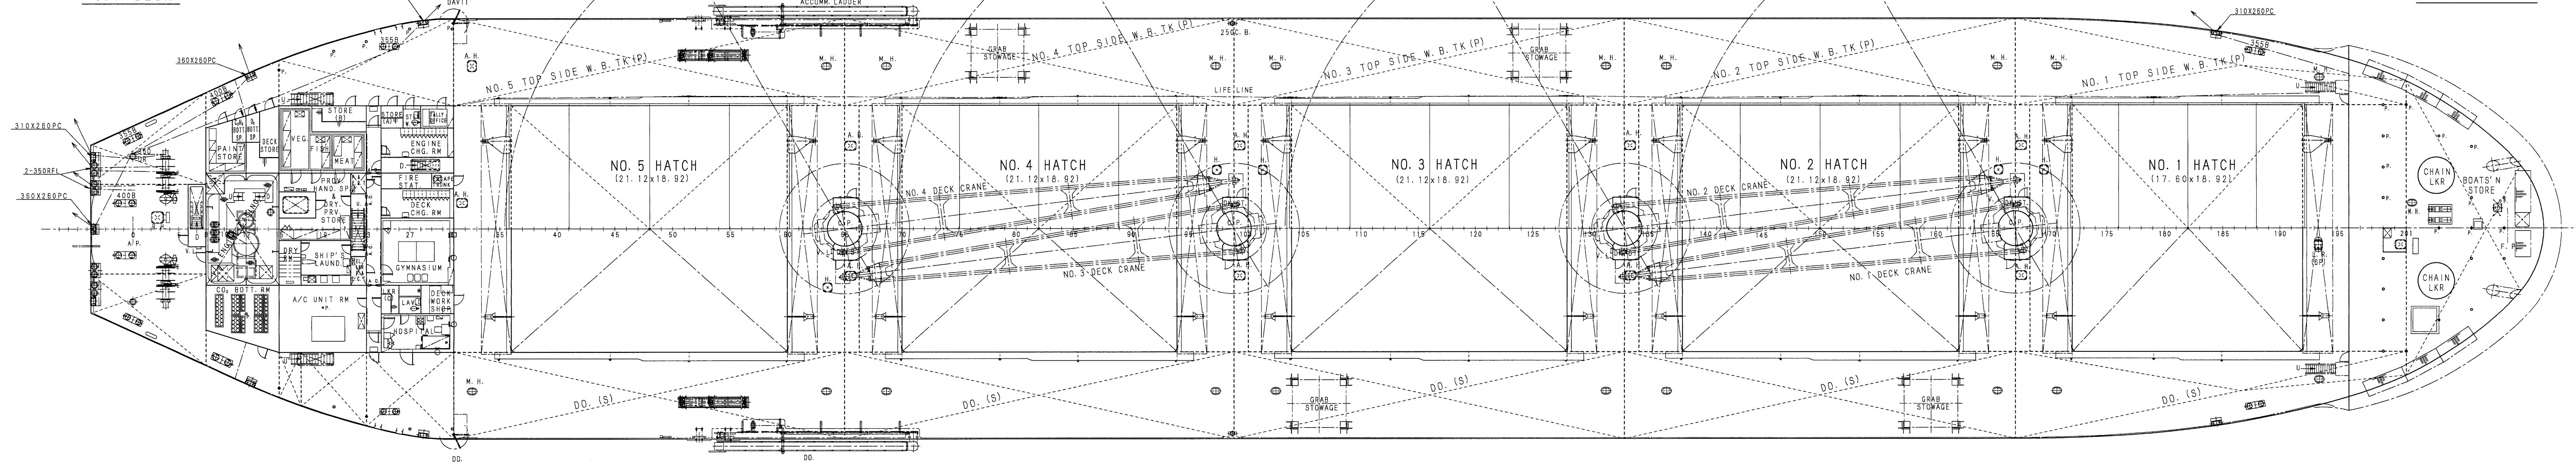
NO. 5 HATCH
NO. 4 HATCH
NO. 3 HATCH
NO. 2 HATCH
NO. 1 HATCH
NO. 4 DECK CRANE
NO. 3 DECK CRANE
NO. 2 DECK CRANE
NO. 1 DECK CRANE
ACCOMM. LADDER
CHAIN LKR
BOATS'N STORE

F'CLE DECK

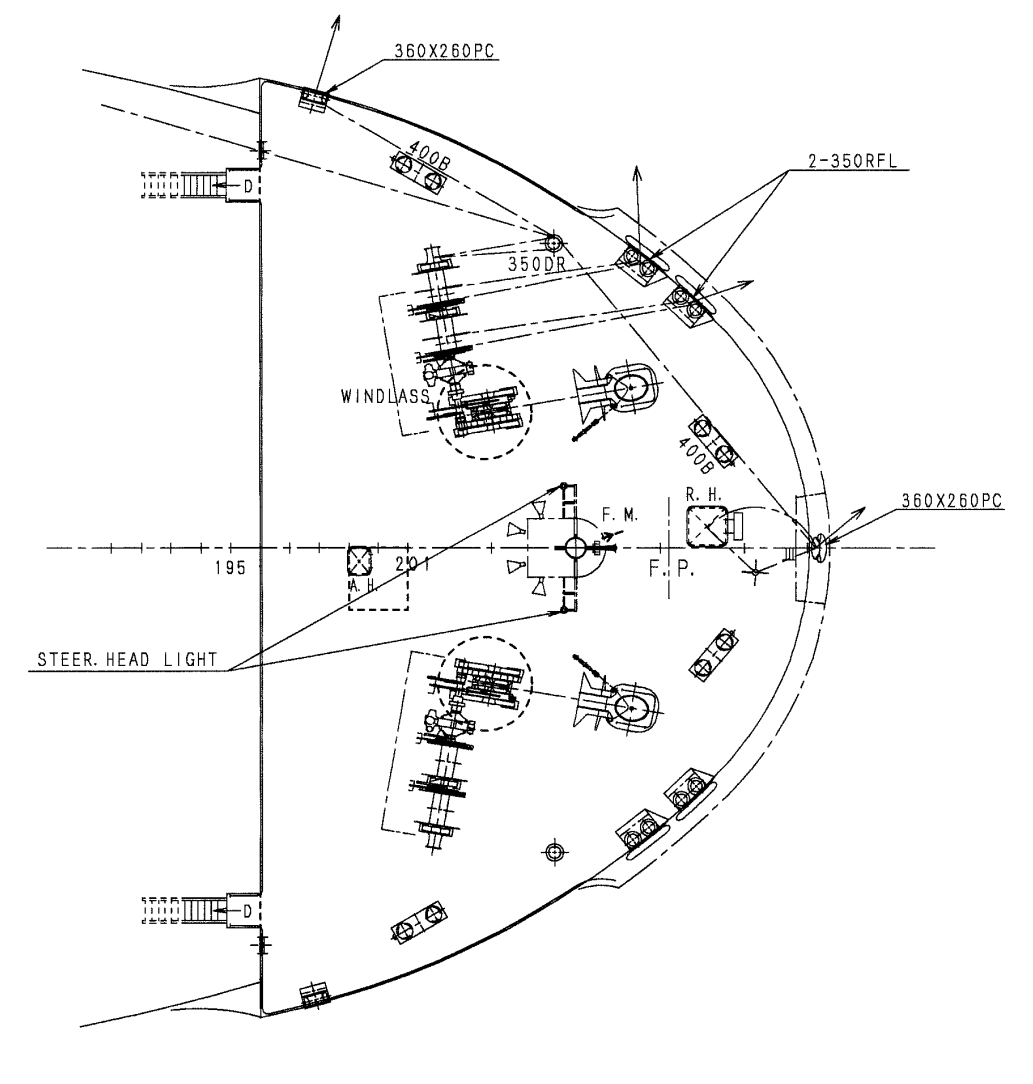
STEER. HEAD LIGHT

2ND. DECK

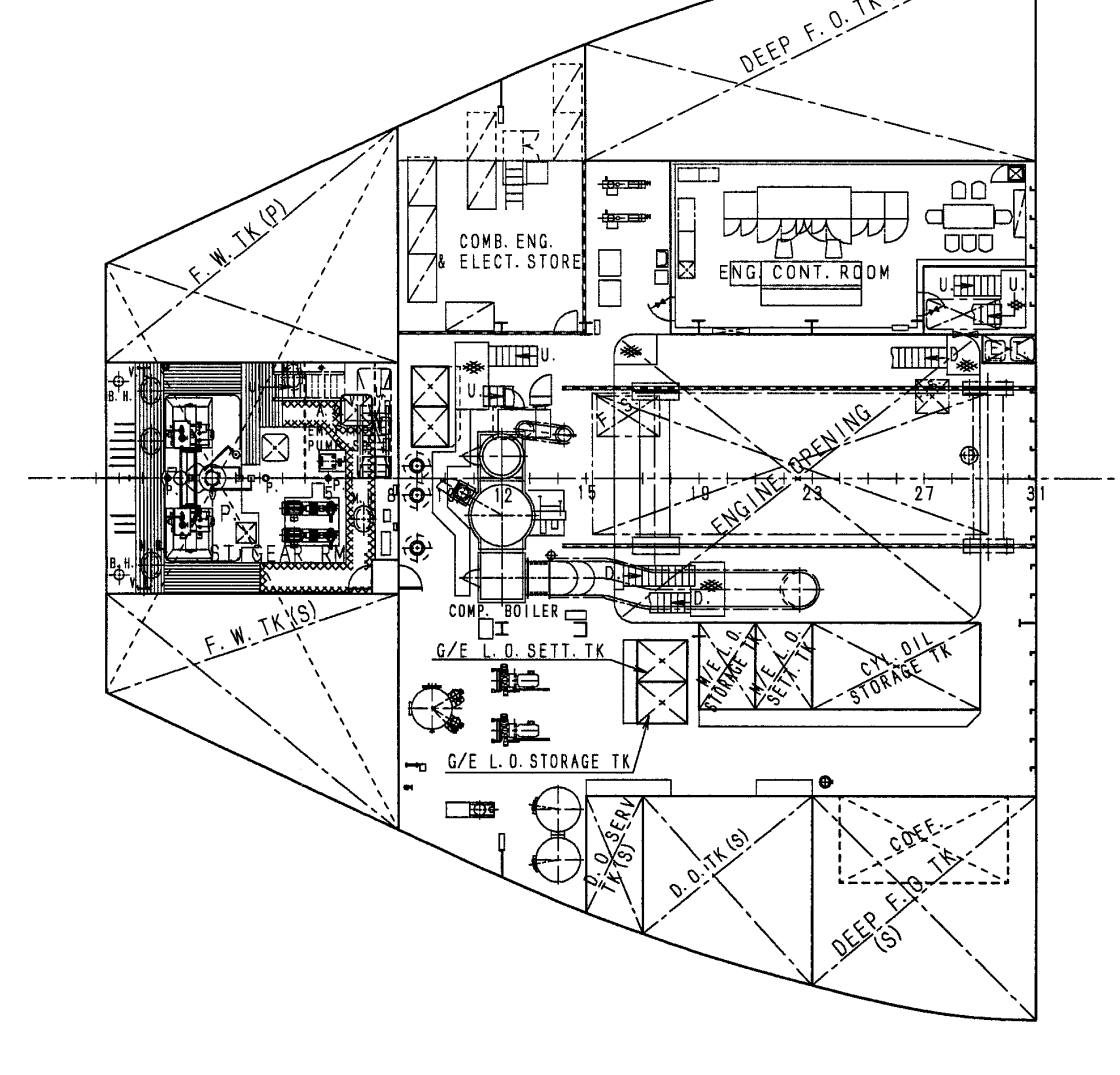

3RD. DECK

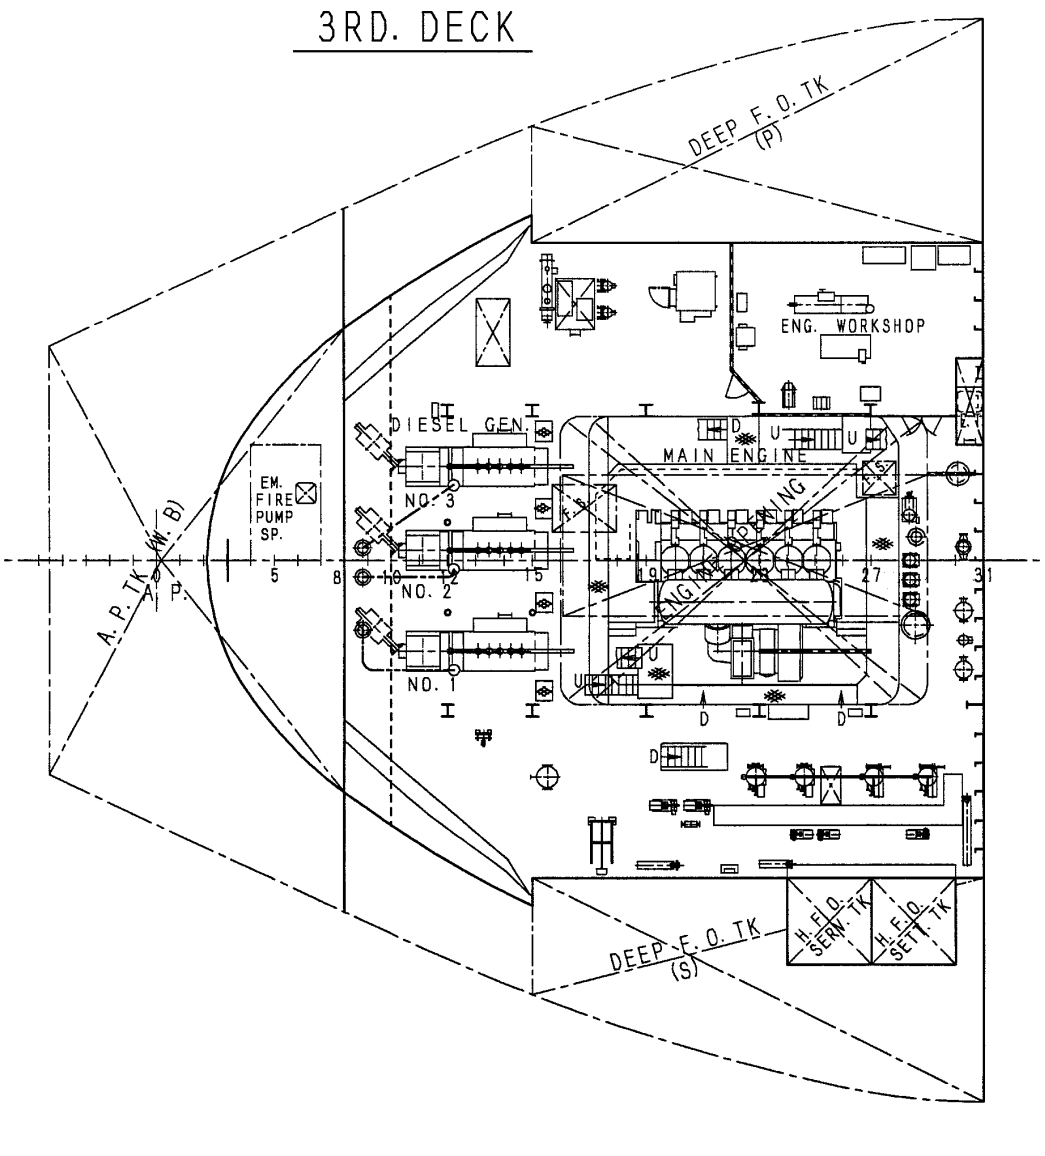

TANK TOP

HOLD

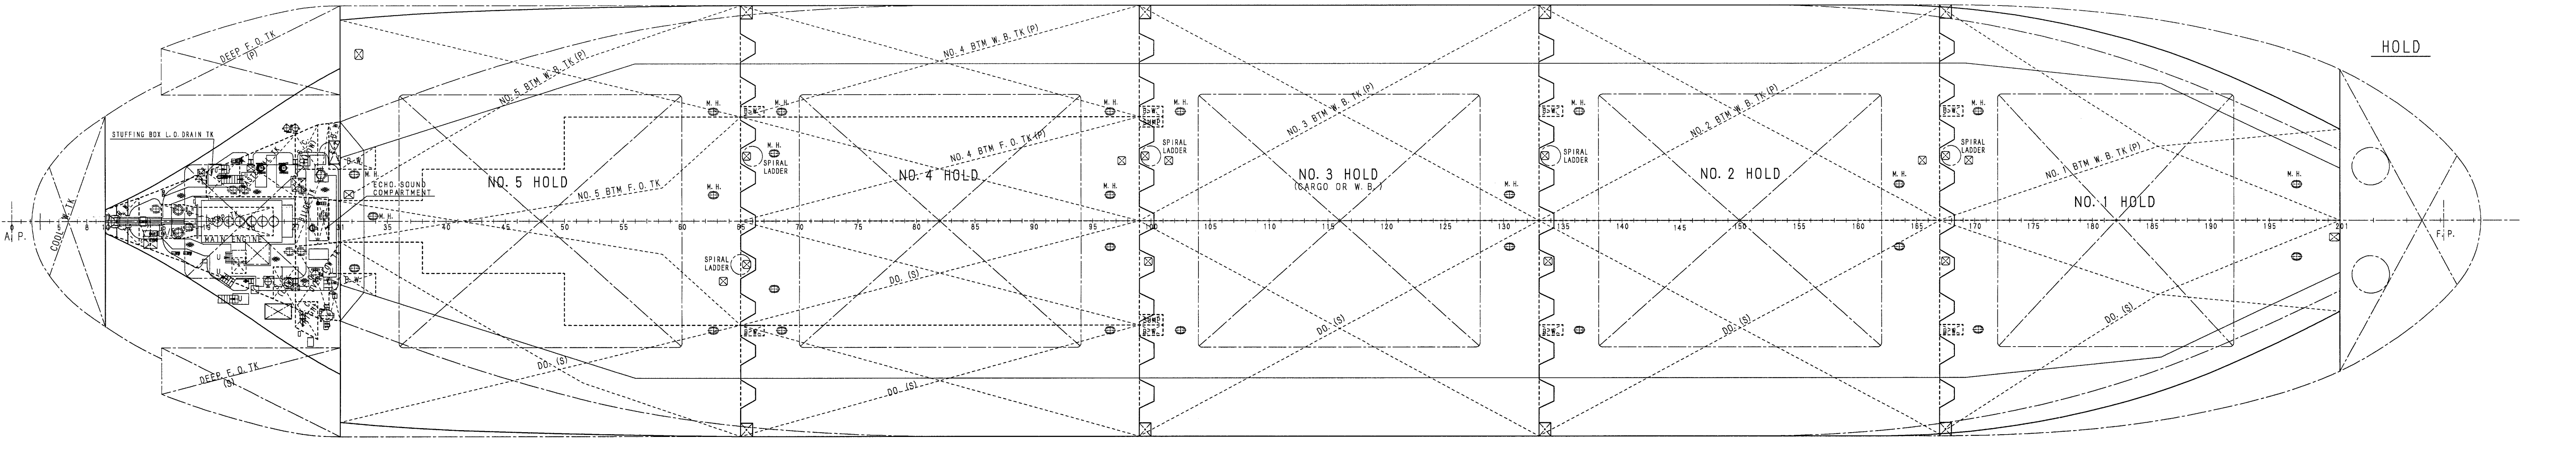
NO. 5 HOLD
NO. 4 HOLD
NO. 3 HOLD
NO. 2 HOLD
NO. 1 HOLD
A.P.
F.P.

THE INFORMATION SHOWN ON THIS DRAWING OR DOCUMENT IS THE EXCLUSIVE PROPERTY OF MES. YOU ARE REQUESTED TO HANDLE IT IN STRICT CONFIDENCE. IT MUST NOT BE USED COPIED OR REPRODUCED WITHOUT THE EXPRESS PERMISSION OF MES.

FINISHED PLAN

MITSUI ENGINEERING & SHIPBUILDING CO., LTD.
TAMANO WORKS

BASIC DESIGN DEPARTMENT GENERAL MANAGER	SHIP'S NO. **S. No. 1592**	SHIP'S NAME **HELENE SELMER**
PROJECT MANAGER	D.W. 56,000 M.T. TYPE BULK CARRIER 一般配置図 GENERAL ARRANGEMENT	
MANAGER		
ASSIST. MANAGER		
CHARGE ENG'R		
DRAWER 小野		
DATE 28TH FEB., 2005		

JOB NO.	JOBCLASSIF. NO.	SCALE	DRAWING NO.
TS1592		**1/200**	**1KDGG01**
			LIST NO. **HA-02**

TO LIST